



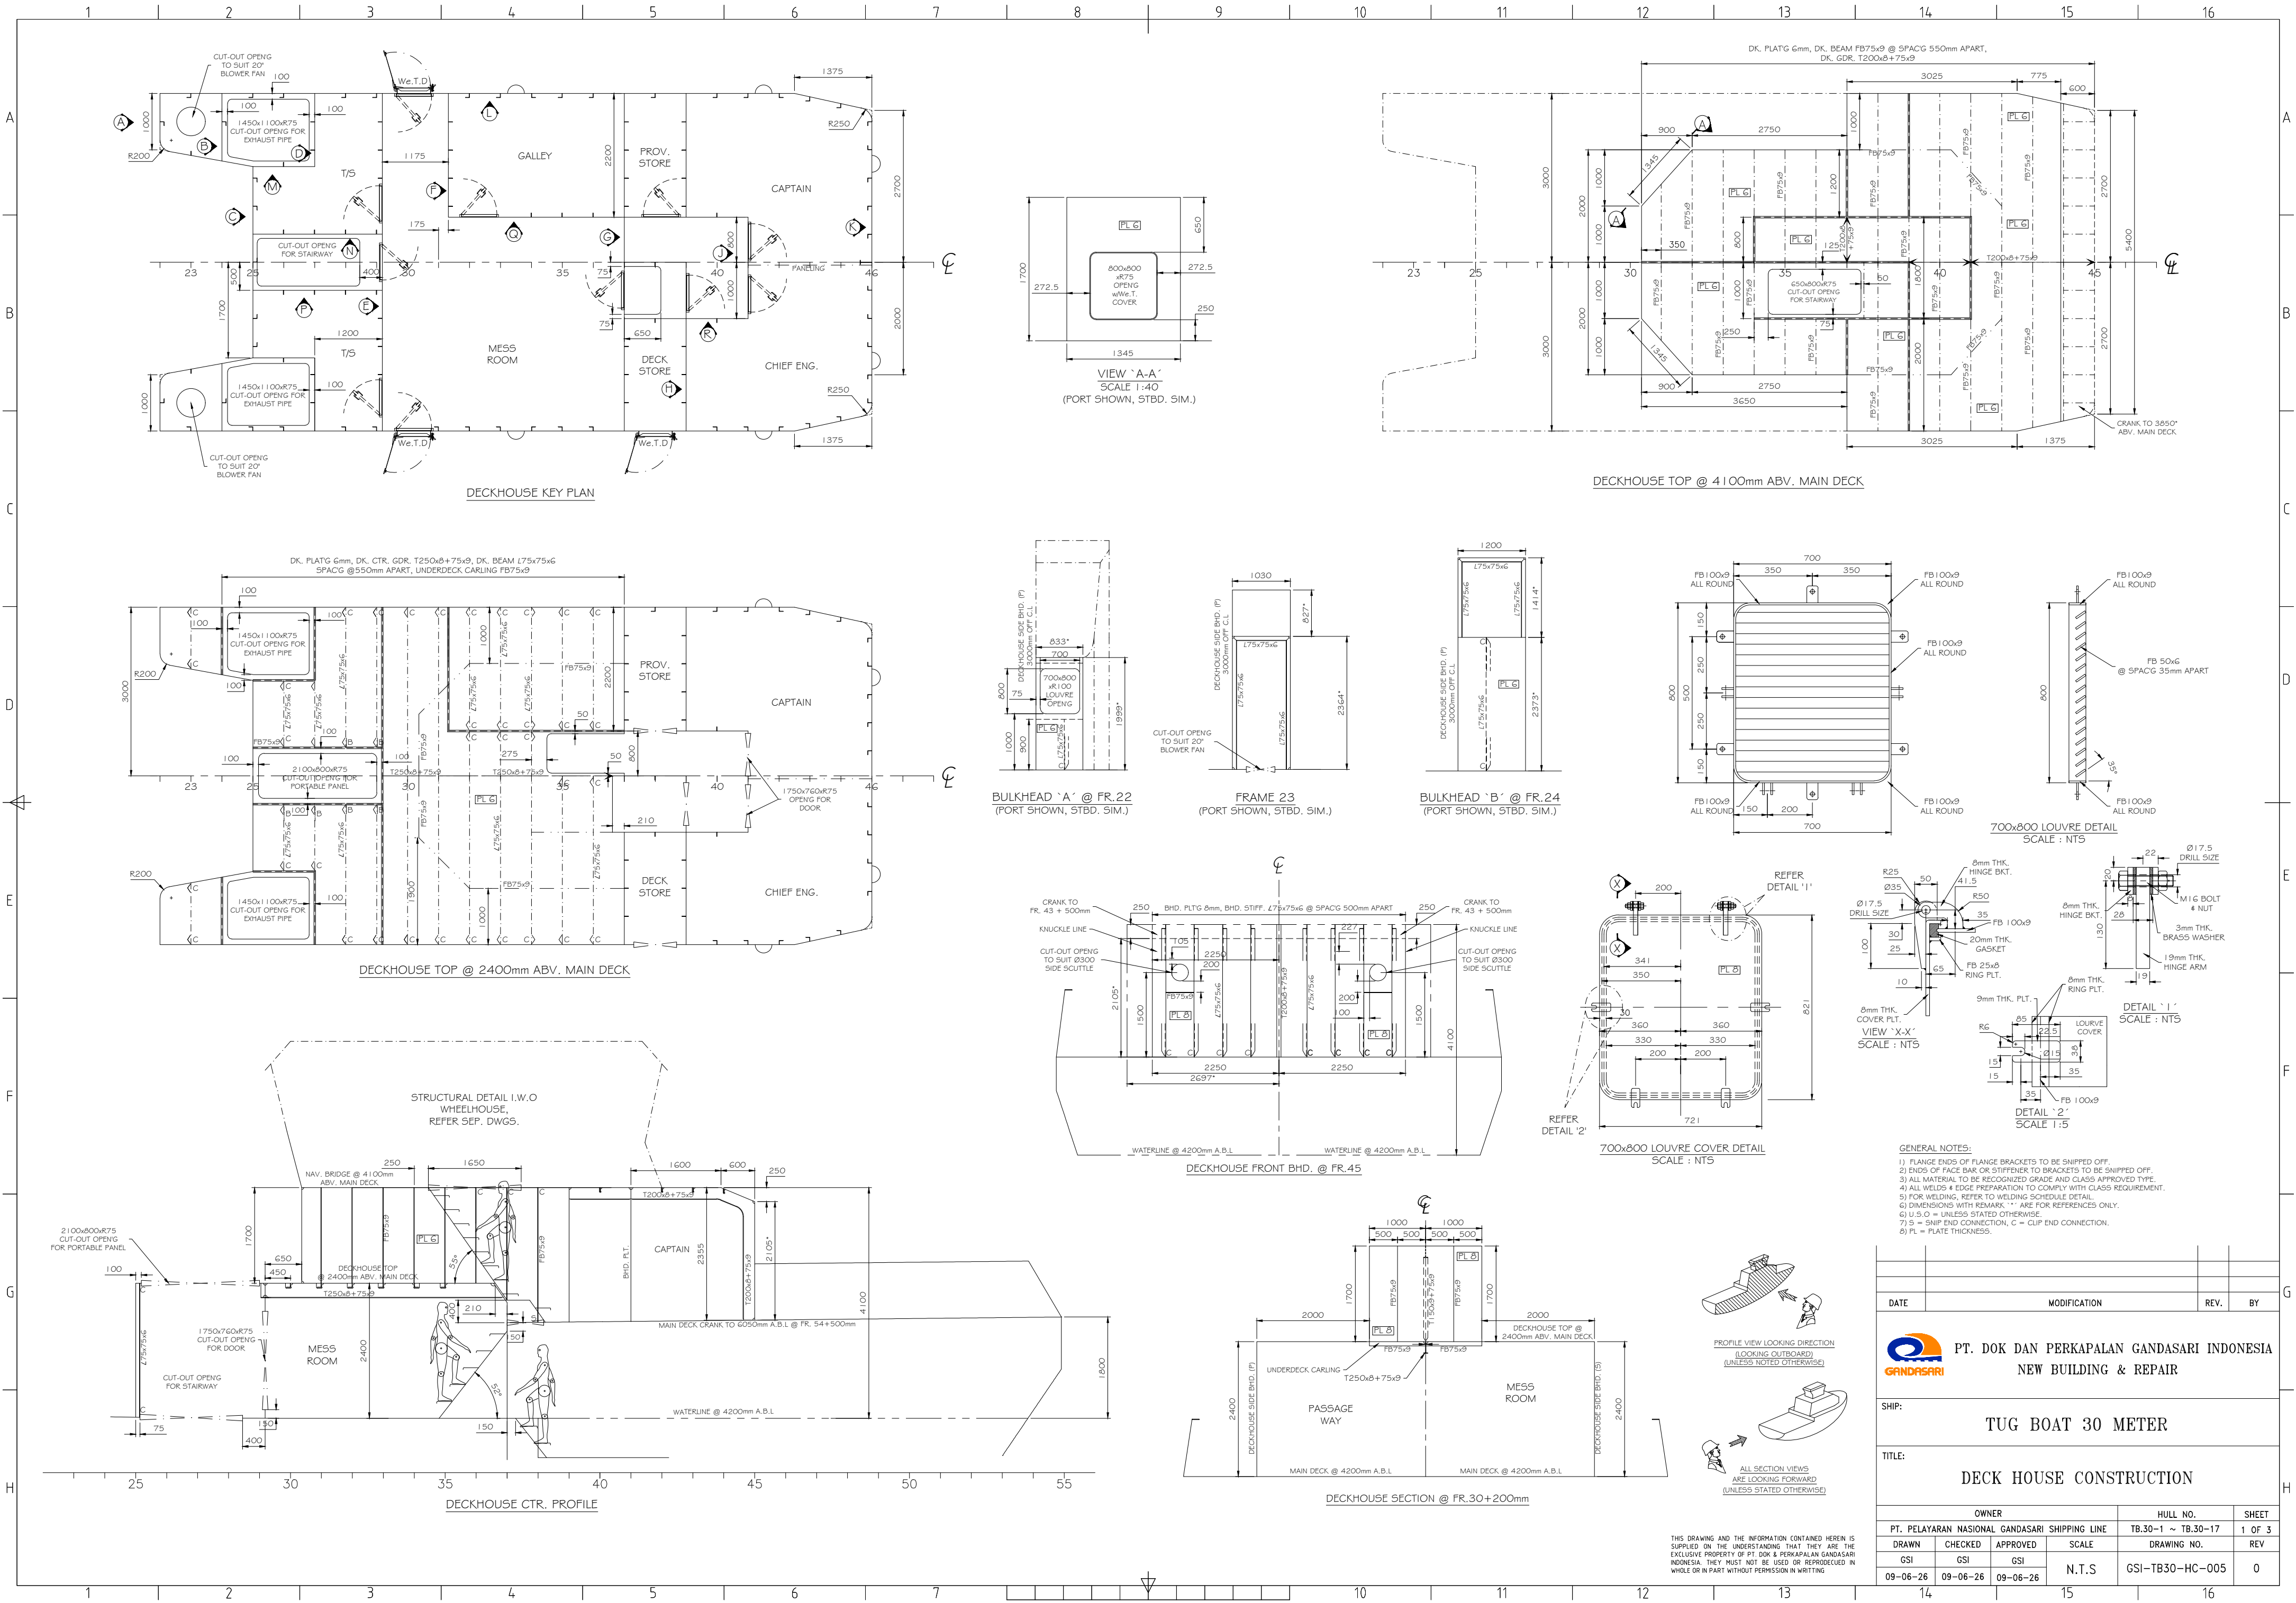



| DATE                                                                | MODIFICATION | REV.               | BY              |
|---------------------------------------------------------------------|--------------|--------------------|-----------------|
| PT. DOK DAN PERKAPALAN GANDASARI INDONESIA<br>NEW BUILDING & REPAIR |              |                    |                 |
| SHIP: TUG BOAT 30 METER                                             |              |                    |                 |
| TITLE: DECK HOUSE CONSTRUCTION                                      |              |                    |                 |
| OWNER                                                               |              | HULL NO.           | SHEET           |
| PT. PELAYARAN NASIONAL GANDASARI SHIPPING LINE                      |              | TB.30-1 ~ TB.30-17 | 2 OF 3          |
| DRAWN                                                               | CHECKED      | APPROVED           | SCALE           |
| GSJ                                                                 | GSJ          | GSJ                | N.T.S           |
| 09-06-26                                                            | 09-06-26     | 09-06-26           | GSJ-TB30-HC-005 |
|                                                                     |              |                    | REV             |
|                                                                     |              |                    | 0               |

THIS DRAWING AND THE INFORMATION CONTAINED HEREIN IS SUPPLIED ON THE UNDERSTANDING THAT THEY ARE THE EXCLUSIVE PROPERTY OF PT. DOK & PERKAPALAN GANDASARI INDONESIA. THEY MUST NOT BE USED OR REPRODUCED IN WHOLE OR IN PART WITHOUT PERMISSION IN WRITING.

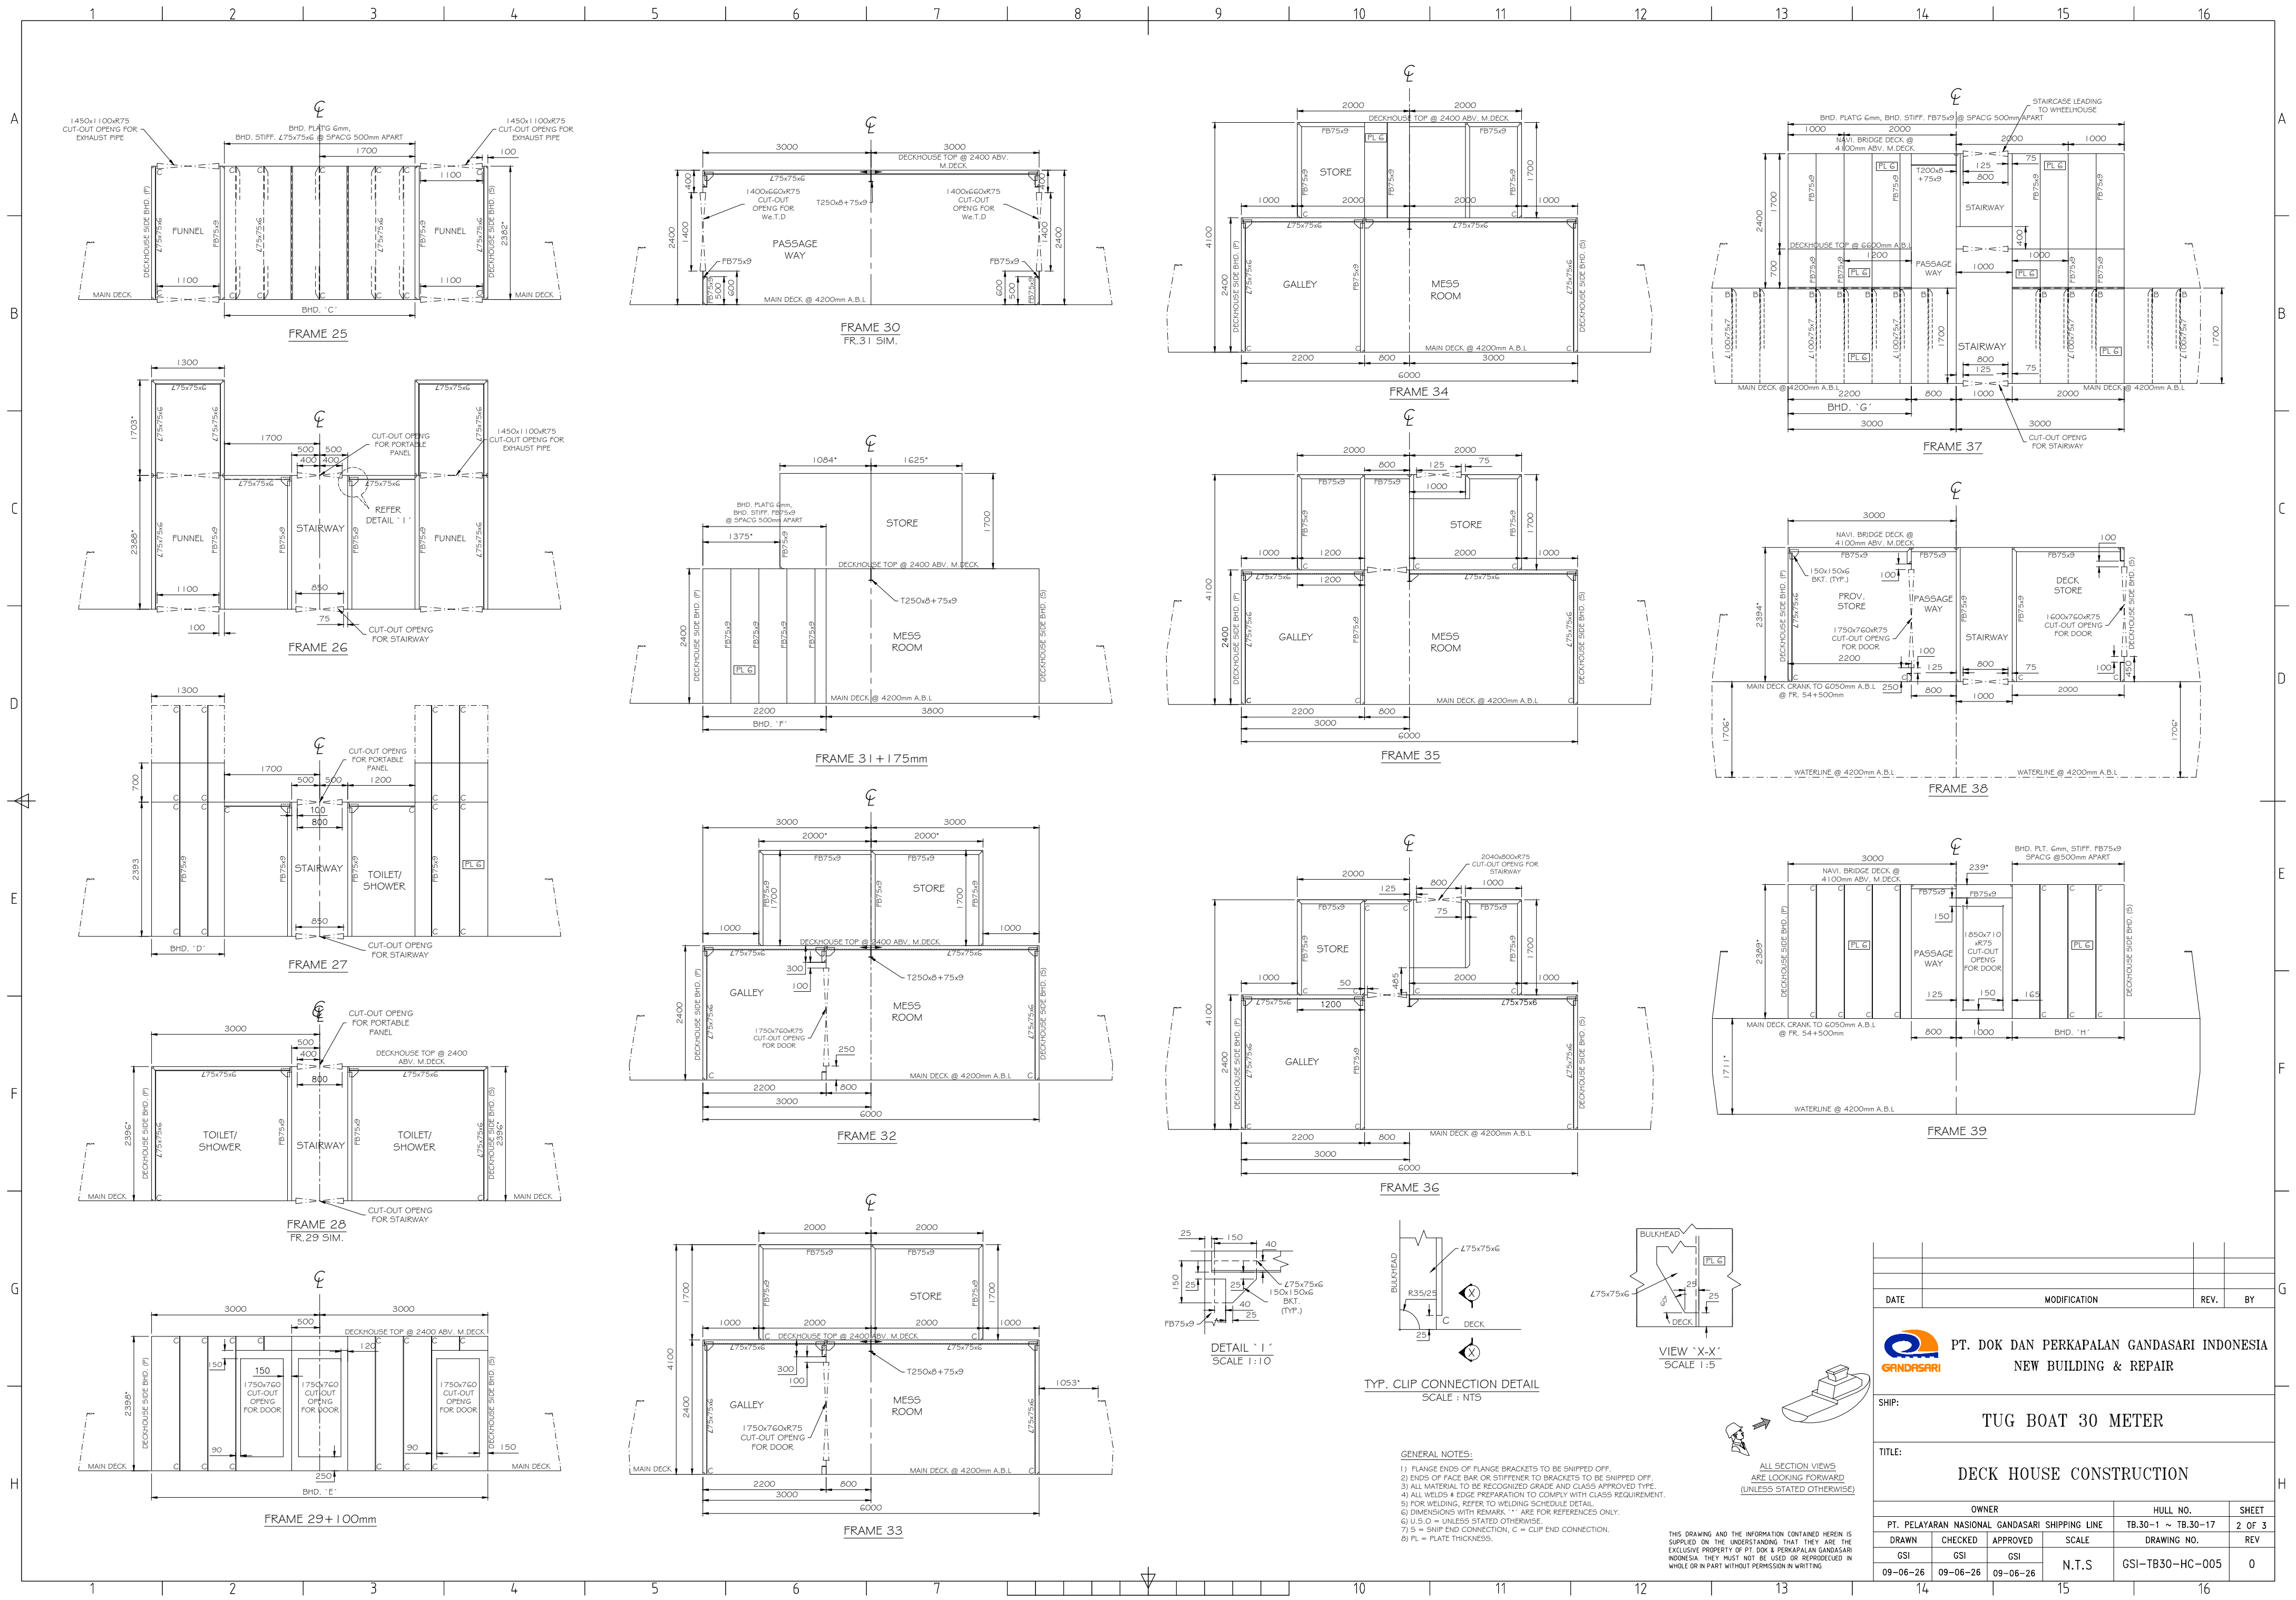

